




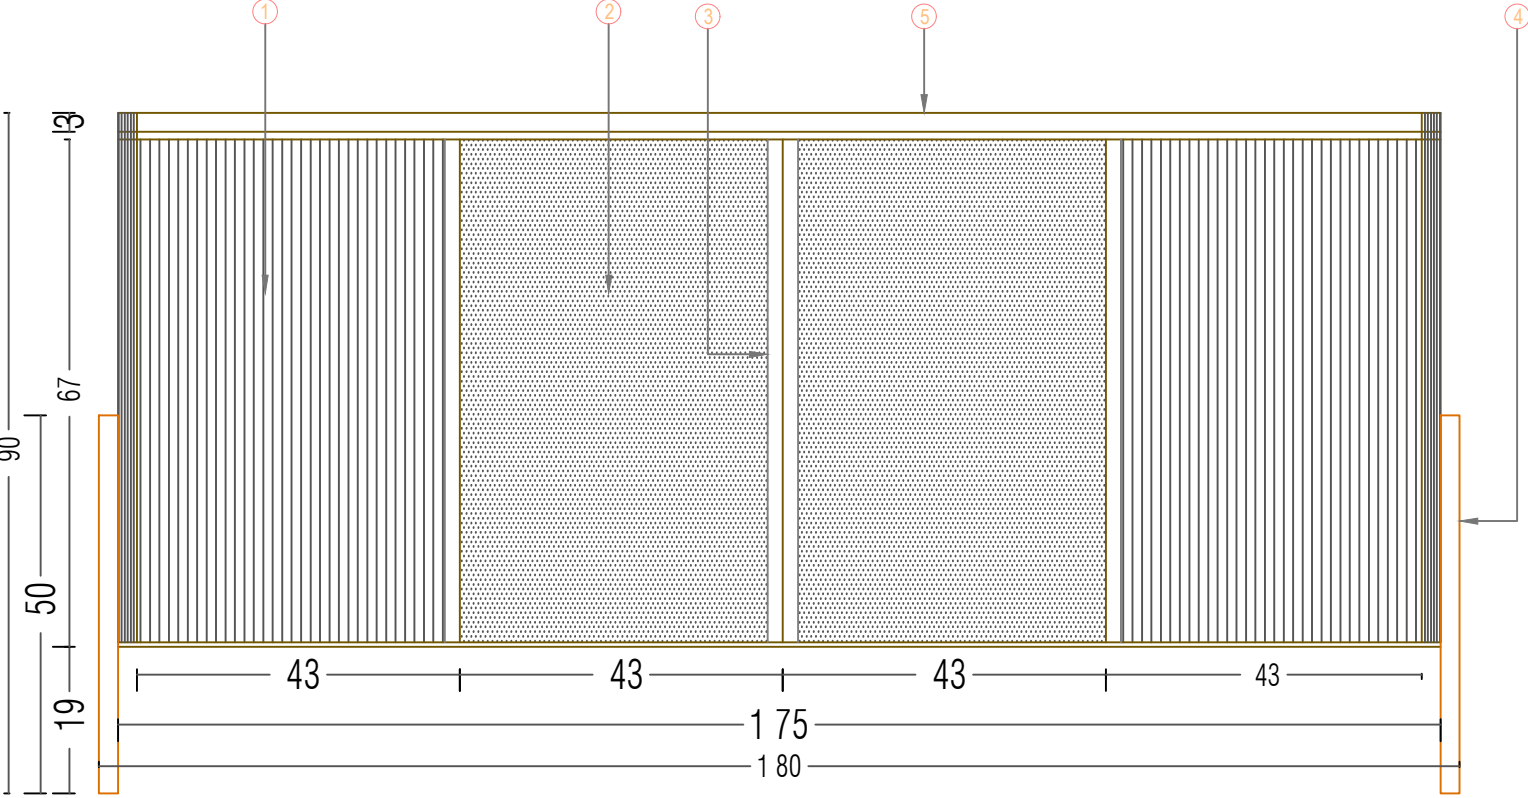


ELEVATION

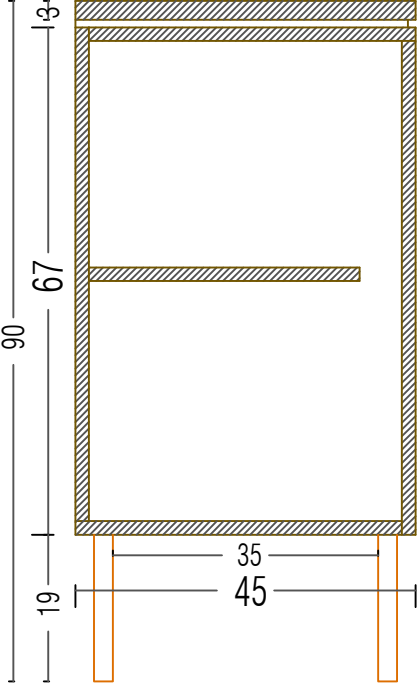

SECTION

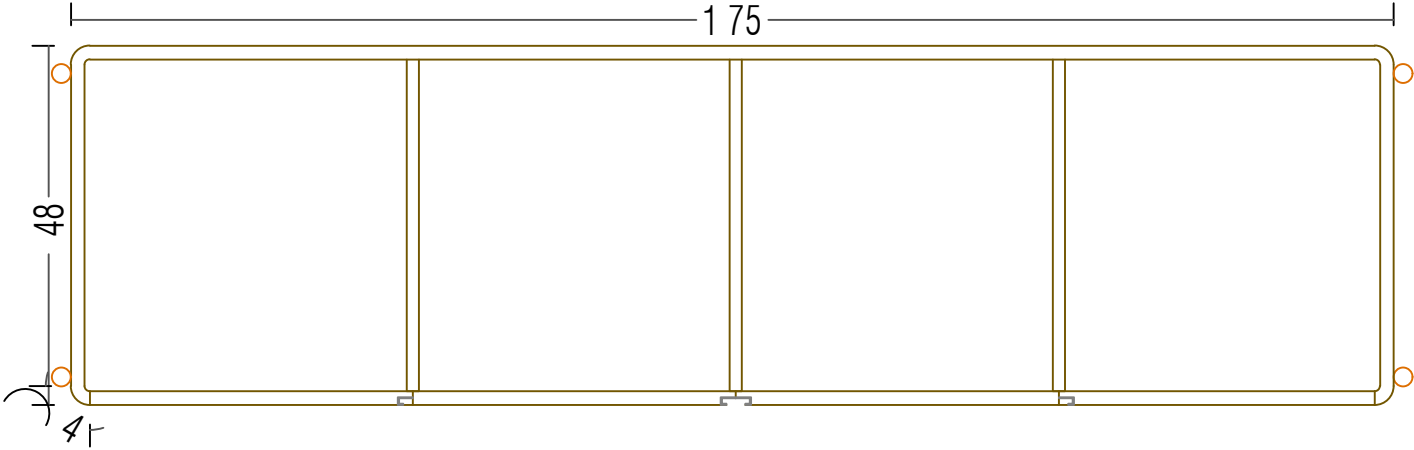

PLAN

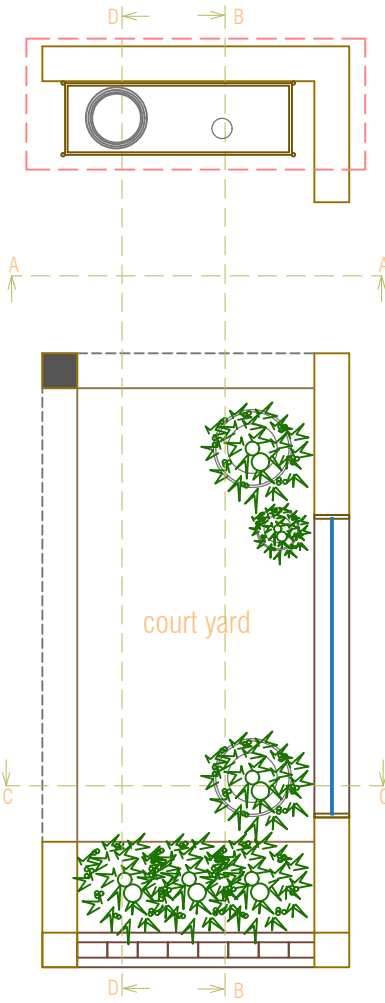

PLAN

SL NO	DESCRIPTION
1	16 MM PLYWOOD (TROJAN) DOOR WITH LAMINATION FINISH (FL 64 SEQUENCE)
2	16 MM PLYWOOD (TROJAN) DOOR WITH LAMINATION FINISH (SUD 5566 GREENLAM)
3	PROFILE HANDLE
4	1/2" MS ROD LEG GOLDEN FINISH
5	TOP MARBLE