

INTERIOR ARCHITECTURE & SPATIAL DESIGN

FAIHA FAISAL

*"Translating human social dynamics, cultural context,
and sensory rituals into enduring, warm architectural
environments."*

RESIDENTIAL · COMMERCIAL · BESPOKE JOINERY · FAÇADES



ARCHITECTURAL FACADE & LANDSCAPE



ABOUT THE DESIGNER

Bridging Human Behavior & *Spatial Harmony*

Born and raised in Kerala, India, and now practicing as an interior designer in Calicut, my design foundation is deeply informed by cultural context, natural materials, and an innate focus on how people genuinely experience physical space.

Prior to spatial design, I completed a **Bachelor's degree in Sociology from Calicut University**. While sociology and interior architecture are often viewed as distinct disciplines, this analytical background fundamentally directs my practice: it empowers me to observe family dynamics, functional flows, and social rituals before drawing a single wall. Wanting to merge that human-centered insight with creative execution, I pursued and completed my **Diploma in Interior Design from Alagappa University**.

Having contributed to residential and commercial projects at *Theyyampattil Homesoul Interior* and *AlHawaj Architect & Builders*, I enjoy guiding projects from early research, conceptual moodboards, and spatial planning through photorealistic 3D visualization and millimeter-accurate technical documentation.

01 · SOCIO-SPATIAL ANALYSIS

Translating user routines and social rituals into organic floor flow and intuitive zoning.

02 · BESPOKE JOINERY CRAFT

Millimeter-level millwork drafting with integrated LED coves and Blum mechanical hardware.

03 · PHOTOREALISTIC 3D RENDERING

Light temperature simulation (2700K–4000K) and tactile material fidelity in Enscape & 3ds Max.

PROFESSIONAL EXPERIENCE SNAPSHOT

Junior Interior Designer · AlHawaj Architect & Builders
Theyyampattil Homesoul Interior · Calicut, Kerala

Space planning, residential villa conceptualization, client presentations, and site supervision.

EDUCATION & CREDENTIALS

Diploma in Interior Design
Alagappa University (2024–2025)

B.A. in Sociology
Calicut University (2017–2020)

CORE SPECIALIZATIONS

Residential Interiors · Space Planning · Photorealistic 3D Visualization · Custom Joinery · Biophilic Courtyards

CALICUT, KERALA

"My background in sociology taught me to observe human rituals and translate them into enduring, emotionally resonant spatial systems."

INDEX OF TYPOLOGIES

Selected Works Contents

01 BEDROOM SANCTUARIES & SUITES Designs 01–03 & Views 01–05 Master Lounges, Arched Niches & Millwork	p. 04–10
02 COURTYARD & BIOPHILIC SPACES Designs 01–03 Modern Zen, Tropical Atrium & Concrete Light Wells	p. 11–13
03 EXTERIOR ARCHITECTURE Villa Facades, Climate Modulation & Framed Overhangs	p. 14
04 CULINARY ARCHITECTURE Designs 01–04 Modular Kitchens, Islands & Blum Hardware	p. 15–18
05 LIVING ENVIRONMENTS Designs 01–03 Double-Height Lounges, Social Flow & Paneling	p. 19–21
06 DINING ARCHITECTURE Entertaining Hubs, Custom Buffet Joinery & Ambient Lighting	p. 22
07 WELLNESS WASHROOMS Master Spa Sanctuary, Soaking Tub, Fluted Stone & Powder Suites	p. 23–24
08 COMMERCIAL WORKPLACE Executive Conference Hall, Boardroom AV Integration & Acoustic Millwork	p. 25
09 TECHNICAL WORKING DRAWINGS Hand-Drawn Ideation & AutoCAD Construction Sets A101–J204	p. 26–32
10 CURRICULUM VITAE & TOOLKIT Professional Experience, Technical Skills & Contact	p. 33

DESIGN METHODOLOGY

The 4-Stage Lifecycle

01 · DISCOVERY & SPATIAL STRATEGY Engaging closely with client lifestyles, cultural habits, circulation constraints, and site context to define the design compass.	BRIEF & RESEARCH
02 · CONCEPT DESIGN & 3D MODELING Synthesizing moodboards, spatial zoning diagrams, material palettes, and photorealistic 3D mockups in SketchUp & 3ds Max.	VOLUME & MOOD
03 · TECHNICAL DETAILING & DOCUMENTATION Producing complete construction packs, electrical schematics, custom joinery sections, and finish schedules with zero ambiguity.	AUTOCAD & REVIT
04 · SITE COORDINATION & REALIZATION Collaborating on-site with carpenters, contractors, and lighting specialists to ensure precision craft and harmonious aesthetic finish.	ON-SITE CRAFT

PRIVATE SANCTUARIES · DESIGN 01

Bespoke Woodcraft, Cane Weave & Dressing Foyer

Conceived as an intimate sanctuary of natural craftsmanship, Design 01 pairs rich teak woodwork, woven cane screening, and organic botanical artwork.

A bespoke bed frame featuring an integrated slatted and woven cane headboard anchors the sleeping volume, while an artisanal carved arched mirror in the dressing foyer establishes deep visual perspective and connects the arrival threshold with rest quarters.

MATERIALITY & ARCHITECTURAL FINISHES

- Woven Natural Cane
- Solid Plantation Teak
- Earthy Lime Wash
- Brushed Brass
- Sisal Weave Rug
- Fluted Timber

SPATIAL & TECHNICAL HIGHLIGHTS

- Hand-woven cane headboard modulating acoustic reverberation and tactile warmth
- Symmetrical bedside floating drawer units with concealed cable management
- Dressing corridor portal with arched artisanal vanity mirror and warm 2700K illumination

TYPOLOGY

Master Suite & Dressing Foyer

HEADBOARD

Custom Teak & Natural Cane

WALL FINISH

Earthy Lime Wash & Botanical Art

FLOORING

Polished Limestone & Sisal Rug

Spatial Reflection: The carved arched mirror in the dressing corridor captures soft natural daylight and reflects the primary bed elevation, cultivating continuous spatial dialogue between morning preparation and restful retreat.



PRIMARY SUITE COMPOSITION · SLATTED CANE HEADBOARD & BOTANICAL TRIPTYCH



DRESSING FOYER & ARCHED MIRROR ELEVATION · SPATIAL CONNECTION & VANITY

PRIVATE SANCTUARIES · DESIGN 02

Warm Minimalist Luxury & Organic Textures

Conceived as an expansive luxury master sanctuary, Design 02 harmonizes tactile natural finishes, architectural lighting, and an integrated private window lounge.

A bespoke timber frame with curved woven cane headboard anchors the bedroom space, while floor-to-ceiling sheer drapery, sculptural hanging globe pendants, and acoustic 3D wall art cultivate an enveloping, resort-grade tranquility.

MATERIALITY & ARCHITECTURAL FINISHES

- Smoked Oak Paneling
- Calacatta Marble Slabs
- Textured Bouclé
- Concealed Cove LED
- Brushed Nickel
- Polished Stone

SPATIAL & TECHNICAL HIGHLIGHTS

- Full-height architectural smoked oak paneling establishing deep visual calm
- Integrated cantilevered window daybed lounge framing tranquil external garden vistas
- Seamless flush door integration connecting the sleeping chamber to the luxury dressing suite


TYPOLOGY
Master Suite & Lounge

HEADBOARD
Custom Timber & Woven Cane


PALETTE
Warm Greige, Teak, Bouclé

FLOORING
Polished Architectural Terrazzo


Spatial Strategy: An open corridor naturally leads to the walk-in wardrobe dressing suite, preserving generous circulation and calm visual breathing room.

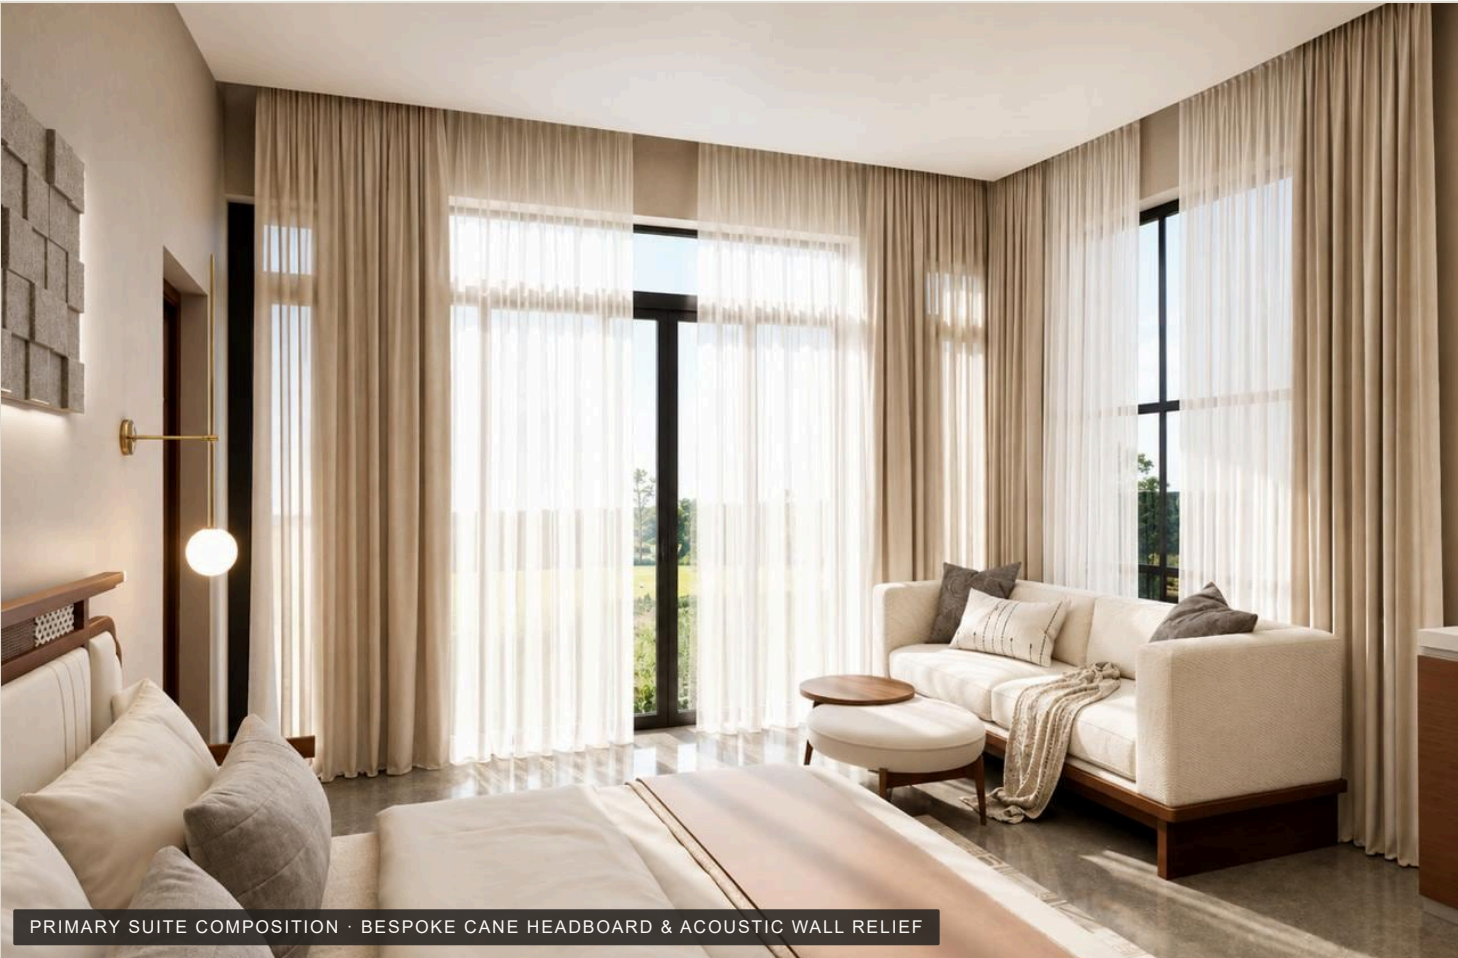

PRIMARY SUITE COMPOSITION · BESPOKE CANE HEADBOARD & ACOUSTIC WALL RELIEF

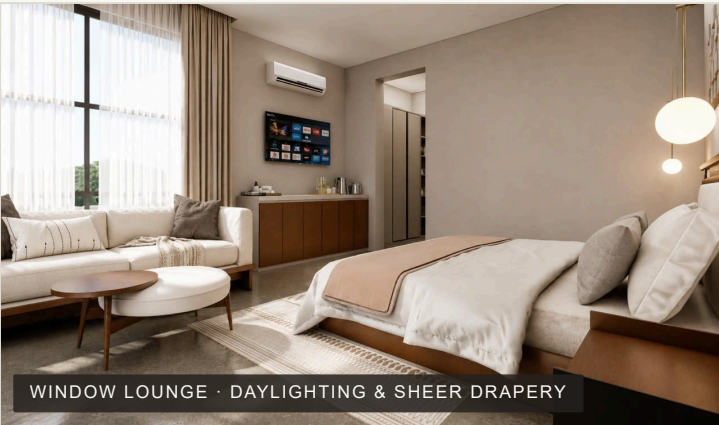

WINDOW LOUNGE · DAYLIGHTING & SHEER DRAPERY

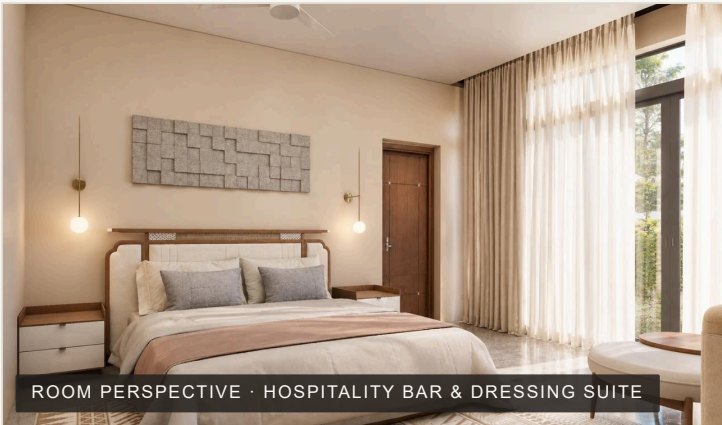

ROOM PERSPECTIVE · HOSPITALITY BAR & DRESSING SUITE

PRIVATE SANCTUARIES · DESIGN 03

Illuminated Arched Niches, Stucco & Vanity Alcove

Conceived as a serene contemporary haven, Design 03 pairs an illuminated sage green stucco arched niche, classical damask wall coverings, and an acoustic perforated plaster frieze.

A low-profile upholstered bed is flanked by minimalist walnut nightstands and dual spherical brass wall sconces. Seamless full-height glazing welcomes abundant daylight and lush garden views, while the dedicated dressing nook integrates an arched vanity mirror and compact floating joinery.

MATERIALITY & ARCHITECTURAL FINISHES

- Backlit Sage Stucco
- Perforated Plaster Frieze
- Natural Walnut Millwork
- Brushed Brass Sconces
- Classical Damask Fabric
- Honed Limestone

SPATIAL & TECHNICAL HIGHLIGHTS

- Symmetrical headboard wall with concealed 2700K perimeter LED radiance
- Dedicated vanity niche creating continuous architectural dialogue with sleeping quarters
- Acoustic perforation frieze mitigating flutter echoes and ensuring restful sanctuary

TPOLOGY

Master Suite & Vanity Nook

ACCENT NICHE

Backlit Sage Stucco Arch

HEADBOARD WALL

Perforated Plaster Frieze

HARDWARE & LIGHTING

Brass Sconces & Warm LED

Lighting Strategy: Concealed warm perimeter LED illumination around the arched alcove creates soft indirect evening radiance, providing a glare-free architectural focal point that gently dissolves boundary walls.



PRIMARY SUITE PERSPECTIVE · ILLUMINATED ARCHED ALCOVE & PERFORATED FRIEZE



AXIAL ELEVATION · SYMMETRICAL BED WALL & BALCONY ACCESS



VANITY NOOK · ARCHED BRASS MIRROR & DAMASK ACCENT

PRIVATE SANCTUARIES · VIEW 01

Minimalist Warmth & Spatial Symmetry

Designed as a tranquil minimalist haven, View 01 centers on balanced spatial alignment, subtle natural light, and refined modern finishes.

Low-profile platform bedding, integrated bedside ledges, and warm recessed LED illumination establish a calming, uncluttered retreat tailored for evening relaxation and peaceful morning daylight.

MATERIALITY & ARCHITECTURAL FINISHES

- Warm Terracotta Stucco
- Ribbed Timber Paneling
- 2700K Recessed Troffers
- Linen Drapery
- Terrazzo Inset
- Brushed Bronze

SPATIAL & TECHNICAL HIGHLIGHTS

- Double-aspect daylight modulation through sheer linen drapery and deep window returns
- Earthy terracotta accent wall grounding the low-profile upholstered platform bed
- Axial circulation pathway linking bedroom lounge effortlessly to outdoor balcony



MAIN BEDROOM COMPOSITION · SYMMETRICAL ELEVATION & LIGHTING

TYPOLGY

Master Bedroom · View 01

PALETTE

Oatmeal, Ash Wood, Linen


LIGHTING

Circadian Warm LED Coves


JOINERY

Concealed Minimalist Units

Spatial Strategy: Pure geometric lines and neutral surfaces accentuate natural textures, eliminating clutter to create an oasis of rest.

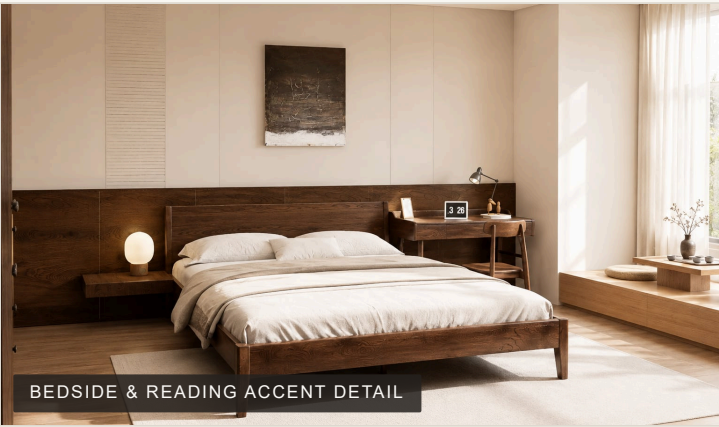

BEDSIDE & READING ACCENT DETAIL

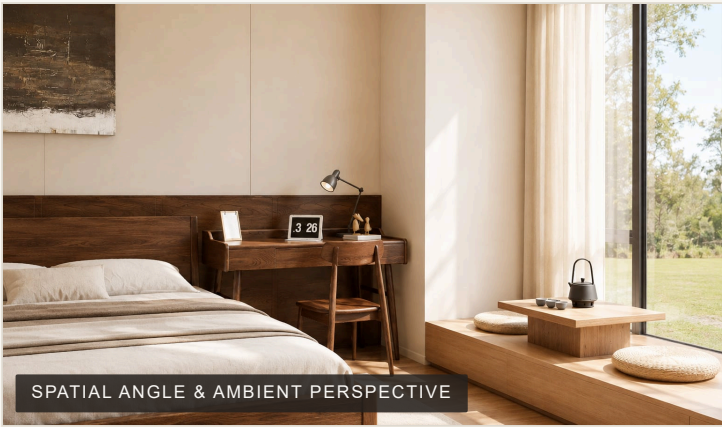

SPATIAL ANGLE & AMBIENT PERSPECTIVE

MASTER SANCTUARY · VIEW 02

Master Suite & Bespoke Millwork

An expansive master bedroom suite featuring an integrated fluted headboard wall panel, full-height custom wardrobe joinery, and an ergonomic vanity study unit.

Acoustic timber battens eliminate flutter echoes while seamlessly housing floating nightstands, touch-activated brass reading sconces, and indirect perimeter illumination.

MATERIALITY & ARCHITECTURAL FINISHES

- Rift-cut White Oak
- Fluted Wall Battens
- Bronze Mirror Glass
- Microcement Flooring
- Blackened Steel Trims
- Wool Felt

SPATIAL & TECHNICAL HIGHLIGHTS

- Unobstructed threshold transition onto private landscaped terrace deck
- Custom floor-to-ceiling wardrobe millwork with flush integrated shadowline pulls
- Directional glare-free architectural reading sconces positioned at ergonomic headboard height

MASTER SUITE BED COMPOSITION & INTEGRATED FLUTED WOOD PANELING

TYPOLOGY

Master Suite · View 02

JOINERY

Full-Height Fluted Wardrobes

MATERIALS

Smoked Walnut, Bouclé, Brass

LIGHTING

Concealed 3000K Perimeter LED

Joinery Focus: Continuous vertical battens maintain architectural rhythm across both bed elevation and dressing alcove, crafting seamless luxury.

WARDROBE SUITE

SLATTED PANELING

VANITY CONSOLE

AMBIENT LIGHTING

ACOUSTIC SANCTUARIES · VIEW 03

Tactile Wood & Organic Warmth

Rooted in organic materials and deep earthy tones, View 03 demonstrates how warm wood textures, acoustic slatted partitions, and tactile linens foster an enveloping sense of quietude.

The spatial configuration balances private sleep zones with reading corners, highlighted by directional warm sconces and soft textured rugs that absorb reverberations.

MATERIALITY & ARCHITECTURAL FINISHES

- Ochre Clay Plaster
- Muted Sandstone Slabs
- Solid Ash Wood
- Warm 3000K Cove Lighting
- Textured Wool Carpet
- Matte Brass

SPATIAL & TECHNICAL HIGHLIGHTS

- Tactile earth-toned plaster finish providing organic natural resonance across all wall faces
- Minimalist closet millwork with concealed reveals and integrated interior sensor lighting
- Axial sightline alignment from arrival threshold through to serene window garden view

TYPOLOGY
Guest Suite · View 03

PALETTE
Moka, Terracotta, Charcoal

TEXTURES
Woven Wool, Slatted Teak

ACOUSTICS
Acoustic Fabric & Battens

Ambiance: Soft perimeter lighting accentuates the organic grain of natural timber, evoking the grounding warmth of a secluded retreat.



MAIN EARTH-TONED SUITE PERSPECTIVE · SLATTING & SOFT FABRICS



ACOUSTIC WALL SLAT DETAIL



TEXTURED LINEN & SCONCE VIGNETTE

ERGONOMIC STORAGE · VIEW 05

Tailored Wardrobe & Study Alcove

View 05 emphasizes space-efficient joinery solutions, featuring custom floor-to-ceiling built-in wardrobes paired with a dedicated vanity console.

Flush handle profiles, integrated LED sensor strips, and compartmentalized organizers maximize functional capacity within a minimal footprint.

MATERIALITY & ARCHITECTURAL FINISHES

- Fluted Glass Sliders
- Anodized Champagne Aluminum
- Italian Leather Pulls
- Velvet Dressing Bench
- Backlit Shelf Rails
- Smoked Oak

SPATIAL & TECHNICAL HIGHLIGHTS

- Modular wardrobe interior with dedicated jewelry drawers, hanging bays, and tie trays
- Curved corner vanity transition maximizing circulation clearance in dressing suite
- Full-height backlit dressing mirror providing true-color CRI>95 illumination

TYPOLOGY

Storage Suite · View 05

JOINERY

Full-Height Built-in Wardrobes

WORKSTATION

Integrated Vanity Study Desk

FINISHES

Anti-Fingerprint Matte Laminate

Storage Maximization: Floor-to-ceiling cabinetry conceals wardrobe essentials behind clean, uniform planes for uninterrupted visual order.



BIOPHILIC SANCTUARIES · DESIGN 01

Modern Zen & Contemplative Silence

Conceived as a contemplative sanctuary within the residence, Design 01 translates classic Japanese zen garden principles into a contemporary architectural form.

Raked white quartz gravel, organic granite stepping pavers, and a Japanese maple focal point are gently illuminated by overhead skylight louvers, inviting shifting sun patterns and serene stillness into daily living.

MATERIALITY & ARCHITECTURAL FINISHES

- White Quartz Gravel
- Honed Granite Stepping Pavers
- Weathered Cedar Decking
- Perforated Breezeway Screen
- Japanese Maple Specimen
- Basalt

SPATIAL & TECHNICAL HIGHLIGHTS

- Geometric water reflection pool with recessed underwater spotlights and granite coping
- Perforated breeze wall modulating harsh afternoon sun while enabling cross-ventilation
- Seamless flush threshold connecting indoor living room directly into open-air courtyard



MODERN ZEN COURTYARD · GRANITE PAVERS & SKYLIT LIGHT ATRIUM

TYPOLOGY Internal Zen Garden	MATERIALS Granite Pavers, White Quartz
FOCAL ELEMENTS Japanese Maple & Basin	DAYLIGHT Filtered North Skylight
Spatial Strategy: Low-profile ground textures and frameless glass thresholds visually expand connecting corridors, transforming circulation into a restful pause.	



RAKED GRAVEL BED & STEPPING PAVER DETAIL



SKYLIGHT PERSPECTIVE & AMBIENT DAYLIGHT FLOW

BIOPHILIC SANCTUARIES · DESIGN 02

Tropical Atrium & Thermal Modulation

Design 02 serves as both a lush green sanctuary and a high-performance thermal chimney, channeling fresh breezes and gentle filtered daylight into the home's core.

A cantilevered timber pergola roof modulates harsh midday sun, casting dynamic geometric shadows while encouraging natural stack-effect convection that flushes warm interior air through upper clerestory vents.

MATERIALITY & ARCHITECTURAL FINISHES

- Basalt Stone Cladding
- Teak Slat Trellis
- Living Fern Wall
- Black Pebble Border
- Frameless Skylight Glazing
- Cast Bronze

SPATIAL & TECHNICAL HIGHLIGHTS

- Double-height glass skylight atrium channeling abundant diffuse northern sunlight
- Integrated automated drip-irrigation vertical plant wall promoting indoor air purification
- Cantilevered natural timber bench seating integrated into the perimeter stone planter



TROPICAL LIGHT ATRIUM · LUSH FOLIAGE & DOUBLE-HEIGHT WELL



CANTILEVERED TEAK PERGOLA & SUNLIGHT MODULATION

TYPOLOGY
Tropical Light Atrium

FLORA
Monstera, Ficus, Tree Ferns

SHADING
Cantilevered Teak Pergola

CLIMATE
Passive Stack Ventilation

Micro-Climate Benefit: High foliage transpiration and sheltered breeze corridors lower adjacent ambient temperatures naturally without artificial mechanical cooling.

BIOPHILIC SANCTUARIES · DESIGN 03

Raw Concrete & Architectural Honesty

Design 03 embraces sculptural minimalism, combining board-formed cast concrete planter walls with custom teakwood bench seating and architectural pebble drainage channels.

Crisp geometric lines frame tactile greenery against smooth cement surfaces, elevated at dusk by discreet recessed 3000K floor grazers that highlight the natural aggregate texture of the walls.

MATERIALITY & ARCHITECTURAL FINISHES

- Board-Formed Concrete
- Reclaimed Ironwood
- River Rock Bed
- Polished Microcement
- Stainless Tension Cables
- Bamboo Shading

SPATIAL & TECHNICAL HIGHLIGHTS

- Monolithic architectural concrete wall featuring authentic timber board grain texture
- Floating raw-edge timber bench hovering above a recessed river pebble drain bed
- Sculptural specimen planting illuminated by low-voltage recessed ground uplights



MONOLITHIC CONCRETE PLANTER & INTEGRATED TEAK SEATING HERO



PLANTER JOINERY



PEBBLE DRAIN CHANNEL



CONCRETE TEXTURE



GROUND ILLUMINATION

TYPOLOGY

Raw Concrete Courtyard

SURFACES

Board-Formed Concrete

JOINERY

Integrated Teak Benches

LIGHTING

Recessed 3000K Ground Grazers

Material Detailing: The tactile contrast between solid board-formed concrete and warm wood grain achieves an enduring, dignified architectural balance.

FACADES & ENTRYWAYS

Tropical Form & Framed Thresholds

The architectural exterior was conceived as a dynamic dialogue between contemporary geometric minimalism and tropical contextual responsiveness.

Deep cantilevered overhangs, integrated green planters, and vertical rhythmic louvers modulate harsh tropical daylight while ensuring effortless cross-ventilation. Bold geometric volumes protect family privacy while crafting a dignified, enduring street presence.

MATERIALITY & ARCHITECTURAL FINISHES

- Cast Concrete Portals
- Marine-Grade Teak Louvers
- Low-E Solar Glazing
- Textured Sand Wash
- Black Powdercoated Aluminum
- Granite

SPATIAL & TECHNICAL HIGHLIGHTS

- Deep structural cantilevered overhangs providing passive solar protection in tropical heat
- Rhythmic vertical timber louvers shielding upper floor bedroom terraces for privacy
- Layered architectural massing defining an impressive yet welcoming private arrival court

TYPOLOGY
Modern Villa Facade

LOCATION
Kerala, India

SOFTWARE
AutoCAD, SketchUp, Enscape

FOCUS AREA
Climate Shading & Massing

Design Intent: Seamless transition between the public arrival approach and private residential retreat through tactile concrete, warm teakwood, and recessed lighting.




MAIN APPROACH ELEVATION · DAYLIGHT STUDY



ENTRY PORCH



CANTILEVER

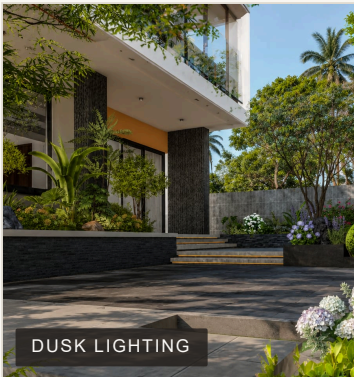

DUSK LIGHTING



BALCONY PLANTER

CULINARY ARCHITECTURE · DESIGN 01

Nordic Minimalism & Streamlined Joinery

Design 01 pairs clean Nordic minimalism with warm oak accents to create an airy, light-flooded culinary workspace. Designed with strict adherence to ergonomic circulation, the island configuration enables fluid multi-person cooking and entertaining.

Concealed handle profiles, anti-fingerprint matte acrylic surfaces, and stain-resistant quartz countertops ensure timeless aesthetic purity paired with effortless day-to-day resilience.

MATERIALITY & ARCHITECTURAL FINISHES

- Ultra-Matte Acrylic
- Natural Oak Veneer
- Calacatta Quartz Slabs
- Brushed Brass Mixer
- Blum Blumotion Slides
- Fluted Tile

SPATIAL & TECHNICAL HIGHLIGHTS

- Ergonomic kitchen working triangle optimizing distances between prep, cooking, and refrigeration
- Continuous quartz waterfall island with flush undermount sink and integrated breakfast seating
- Handleless push-to-open upper cabinets with integrated warm under-cabinet task LED strips

TYPOLOGY
Island Modular Kitchen

PALETTE
Matte White, Oak, Calacatta

COUNTERTOPS
Engineered Quartz Slab

HARDWARE
Blum Tandembox Soft-Close

Spatial Strategy: Low-profile central island maintains clear sightlines into adjacent living zones while doubling as a casual breakfast bar.



KITCHEN ELEVATION & QUARTZ BREAKFAST ISLAND



PANTRY STORAGE & FLUTED JOINERY DETAIL



HOB STATION & AMBIENT LED PROFILE

CULINARY ARCHITECTURE · DESIGN 02

Monolithic Quartz & Textured Cabinetry

Design 02 celebrates bold textural contrast, pairing dark fluted wood cabinetry with a dramatic monolithic waterfall quartz island. The composition anchors the home as an inviting social and culinary centerpiece.

Flush-integrated high-end appliances remain hidden behind full-height smoked oak panels, preserving the pristine architectural massing while delivering uncompromising professional kitchen performance.

MATERIALITY & ARCHITECTURAL FINISHES

- Charcoal Fluted Laminate
- Stainless Steel Backsplash
- Silestone Countertop
- Smoked Glass Cabinets
- Recessed Channel LED
- Matte Black

SPATIAL & TECHNICAL HIGHLIGHTS

- High-capacity full-height pantry towers with internal pull-out tandem storage baskets
- Under-cabinet 3000K warm task lighting completely eliminating worktop shadow zones
- Central prep island housing flush induction cooktop and downdraft ventilation unit

TYPOLOGY

Open-Plan Island Kitchen

ISLAND

Waterfall Quartz Countertop

CABINETRY

Smoked Oak & Fluted Panels

FITTINGS

Matte Gunmetal & 3000K LED

Work Triangle: Prep sink, induction hob, and concealed refrigeration form an effortless golden triangle with zero wasted footsteps.



MONOLITHIC WATERFALL ISLAND & SMOKED WOOD ACCENTS



BREAKFAST BAR COUNTER



CONCEALED APPLIANCE JOINERY



TASK LIGHTING & PREP STATION

CULINARY ARCHITECTURE · DESIGN 03

Parallel Efficiency & Ambient Illumination

Design 03 utilizes a high-efficiency parallel (galley) layout that maximizes functional counter run while accommodating dedicated wet and dry preparation zones.

Warm contemporary timber laminates, anti-glare under-cabinet LED task profiles, and textured stone backsplashes create an intimate, tactile cooking atmosphere tailored for passionate home chefs.

MATERIALITY & ARCHITECTURAL FINISHES

- Bleached Birch Plywood
- Fluted Ceramic Subway Tiles
- Terrazzo Worktops
- Matte Black Fixtures
- Integrated Herb Planters
- Natural Rattan

SPATIAL & TECHNICAL HIGHLIGHTS

- Open timber floating shelves displaying curated tableware with concealed recessed groove lights
- Vertical stacked ceramic subway tile splashback sealed with waterproof epoxy grout
- Concealed countertop appliance garage equipped with bi-fold retracting pocket doors

TPOLOGY

Parallel Modular Kitchen

ZONES

Dedicated Wet & Dry Counters

BACKSPLASH

Seamless Large-Format Tile

LIGHTING

Under-Cabinet 3000K Strip LED

Storage Detailing: Full-height larder units and soft-close pull-out pantries organize kitchen essentials with high volumetric efficiency.



CONTEMPORARY PARALLEL KITCHEN & STORAGE EFFICIENCY



BACKSPLASH TILE & LINEAR TASK LIGHT



FULL ELEVATION & CIRCULATION PATH

CULINARY ARCHITECTURE · DESIGN 04

Compact Geometry & Smart Storage Zoning

Design 04 explores high-density modular joinery tailored for compact urban living, demonstrating that restricted square footage never requires aesthetic or functional compromise.

Every millimeter is optimized with corner carousel pull-outs, integrated spice racks, overhead lift-up Blum Aventos bi-fold cabinets, and sleek undermount appliances.

MATERIALITY & ARCHITECTURAL FINISHES

- Blackened Steel Framing
- Distressed Brick Veneer
- Concrete Quartz Slab
- Reclaimed Elm Timber
- Edison Filament Pendants
- Brass Mesh

SPATIAL & TECHNICAL HIGHLIGHTS

- Ceiling-suspended architectural steel gantry storing stemware and bar accessories
- Heavy-duty prep island integrating under-counter beverage cooler and double pull-out waste bins
- Commercial-grade high-arc pull-down sprayer faucet over deep stainless steel basin



COMPACT MODULAR KITCHEN & CLEAN MODERN GEOMETRY

TYPOLOGY
Compact L-Shaped Kitchen

HARDWARE
Blum Aventos Bi-Fold Lift

STORAGE
Corner Carousel & Pull-Outs

SURFACES
Satin Anti-Scratch Acrylic

Ergonomic Detailing: Continuous work surfaces adjacent to both the hob and sink streamline single-cook meal preparation with total fluidity.



TALL STORAGE UNIT & OVEN TOWER



UNDERMOUNT SINK & MATTE CABINERY



ERGONOMIC WORKFLOW TRIANGLE

LIVING ENVIRONMENTS · DESIGN 01

Sanctuary of *Tactile Warmth*

Conceived as a grand restful heart for family life, Design 01 orchestrates natural light penetration, vertical volume, and acoustic balance within an expansive double-height lounge.

Warm fluted oak paneling, integrated media joinery, tactile linen upholstery, and recessed cove lighting create a calming, grounded ambiance that effortlessly counters the fast pace of modern life.

MATERIALITY & ARCHITECTURAL FINISHES

- Bookmatched Statuario Marble
- Charcoal Acoustic Battens
- Top-Grain Italian Leather
- Brushed Brass Reveals
- Motorized Velvet Drapes

SPATIAL & TECHNICAL HIGHLIGHTS

- Monumental two-story bookmatched marble feature wall housing a flush linear ethanol fireplace
- Custom floating media console with acoustic fabric doors concealing AV components
- Spectacular multi-tier sculptural ring chandelier suspended through the double-height void

TYOLOGY

Double-Height Formal Lounge

MILLWORK

Fluted Oak Feature Wall

MATERIALS

Oak, Bouclé, Travertine

LIGHTING

Indirect 3000K Cove LED

Spatial Strategy: Floor-to-ceiling slatted paneling visually connects the ground floor lounge with the upper gallery, unifying vertical sightlines.



DOUBLE-HEIGHT LIVING VOID & FEATURE MEDIA PANELING



LOUNGE SEATING & COFFEE TABLE ARRANGEMENT



VERTICAL PERSPECTIVE & DAYLIGHT GLAZING

LIVING ENVIRONMENTS · DESIGN 02

Acoustic Paneling & Intimate Flow

Design 02 establishes an intimate, cozy family entertainment sanctuary centered on full-height acoustic timber battens and bespoke low-profile credenza joinery.

Deep natural teak textures absorb sound reverberation while providing seamless concealed storage for audiovisual hardware, resulting in an uncluttered aesthetic of quiet elegance.

MATERIALITY & ARCHITECTURAL FINISHES

Slatted American Walnut

Textured Cream Bouclé

Honed Travertine Coffee Tables

Recessed Wall Sconces

Wool-Silk Area Rug

SPATIAL & TECHNICAL HIGHLIGHTS

- Full-perimeter vertical walnut acoustic paneling cultivating sound dampening and intimacy
- Deep-seated modular sectional sofa layout configured for effortless conversational flow
- Integrated display niches finished in brushed bronze with dimmable perimeter warm wash

TYPOLGY

Family Living Retreat

JOINERY

Concealed Low-Profile Credenza

FINISHES

Natural Teak & Warm Linen

HARDWARE

Push-to-Open Concealed Tracks

Acoustic Focus: Wood battens and textured fabrics eliminate echo, creating an enveloping acoustic environment ideal for cinematic immersion.



TACTILE WOOD PANELING & FLOATING MEDIA CONSOLE HERO



TEXTURED WALL PANELING DETAIL & SIDE SCONCE



CIRCULATION FLOW & CEILING LINEAR LIGHT

LIVING ENVIRONMENTS · DESIGN 03

Social Continuity & Curated Vignettes

Design 03 embraces an open-plan lifestyle, seamlessly connecting the informal living zone with adjacent dining spaces through low-profile modular furniture and unobstructed sightlines.

A bespoke open bookcase unit defines spatial boundaries without solid walls, enriched by warm directional brass sconces and recessed ceiling channels for atmospheric evening hosting.

MATERIALITY & ARCHITECTURAL FINISHES

- Micro-Ribbed Wall Panels
- Polished Botticino Marble
- Brushed Bronze Accents
- Sheer Motorized Blinds
- Smoked Walnut Credenza

SPATIAL & TECHNICAL HIGHLIGHTS

- Curved architectural drop ceiling bulkhead with concealed 2700K perimeter LED ribbon
- Symmetrical twin spherical wall sconces framing the primary artwork and floating console
- Continuous visual and material alignment guiding movement from living lounge toward dining



TYPOLOGY

Open-Plan Contemporary Lounge

SEATING

Modular Deep-Seat Sectional


STORAGE

Integrated Open Bookcase Unit

LIGHTING

Directional Sconces & Profile LED

Zoning Detailing: Low-profile furniture forms maintain natural breeze and visual continuity toward adjacent green light courts and entertaining areas.

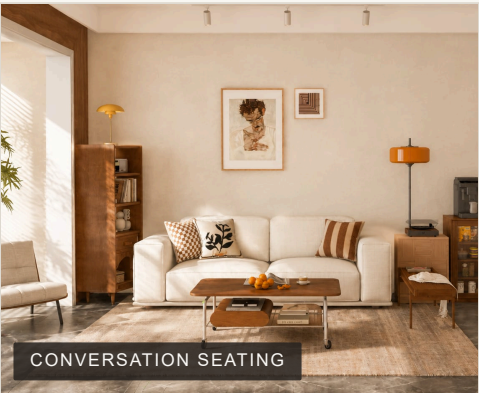

DINING & HOSPITALITY

Social Continuity & Material Harmony

The dining space serves as the central gathering fulcrum connecting the open kitchen with the internal courtyard. It is designed to foster leisurely family meals and gracious evening entertainment.

A bespoke solid timber dining table is flanked by custom upholstered chairs, anchored overhead by a sculptural linear light fixture that emphasizes intimacy without cluttering vertical air space.

MATERIALITY & ARCHITECTURAL FINISHES

- Solid American Walnut
- Fluted Glass Buffet Doors
- Smoked Bronze Mirror
- Brushed Brass Chandelier
- Nubuck Leather Dining Chairs

SPATIAL & TECHNICAL HIGHLIGHTS

- 8-seater monolithic solid timber dining table crafted for grand family hospitality
- Bespoke sideboard buffet credenza featuring fluted glass doors and Calacatta marble counter
- Low-glare architectural pendant luminaire positioned at precise 75cm table datum

TYPOLOGY
Residential Dining Room

SEATING
8-Person Solid Wood Table

CABINETRY
Bespoke Fluted Buffet Unit

FINISHES
Walnut, Brass, Textured Stone

Spatial Strategy: Low-profile furniture forms ensure continuous sightlines toward the green courtyard, weaving nature into everyday dining rituals.



MAIN DINING PERSPECTIVE · TABLE, CHANDELIER & SPATIAL FLOW



CUSTOM BUFFET JOINERY & FLUTED WALL PANELING



LINEAR CHANDELIER & TABLE SETTING VIGNETTE

MASTER EN-SUITE · SPA SANCTUARY

Restorative Calm & Monolithic Stone

Conceived as an immersive private spa retreat within the master residence, the design prioritizes ritual relaxation, natural biophilic connections, and tactile warmth.

A sculptural freestanding soaking bathtub is centered between twin panoramic picture windows framing lush exterior treetops. Bookmatched Calacatta marble wall paneling with an illuminated recessed niche anchors the space, harmonized with fluted white millwork, dark stone flooring, and warm concealed cove illumination.

MATERIALITY & ARCHITECTURAL FINISHES

- Honed Silver Travertine
- Cast Mineral Soaking Tub
- Matte Black In-Wall Taps
- Fluted Natural Oak Vanity
- Frameless Starphire Glass

SPATIAL & TECHNICAL HIGHLIGHTS

- Freestanding sculptural oval soaking tub positioned against full-height lush garden glazing
- Curbless walk-in shower suite featuring ceiling-recessed rainhead and linear slot drain
- Double vanity unit with undermount vitreous china basins and heated anti-fog LED mirror

TPOLOGY

Master Wellness Spa Suite

FEATURE WALL

Bookmatched Calacatta Marble

Biophilic Harmony: Expansive landscape sightlines blend internal sanctuary with outdoor greenery, cultivating an atmosphere of deep restorative tranquility.

BATHTUB

Sculptural Freestanding Tub

FIXTURES

Concealed Brushed Brass & Gunmetal



SECONDARY SUITES & POWDER ROOMS

Tactile Serenity & Precision Detailing

Secondary guest washrooms and powder rooms detailed with uncompromised material discipline and visual calm. Large-format seamless tiles minimize grout joints, maximizing spatial continuity across compact footprints.

Floating stone vanities, ambient halo-lit mirrors, and brushed gunmetal brassware create elegant architectural vignettes. Recessed LED lighting grazes stone textures, eliminating glare while enhancing sensory depth.

MATERIALITY & ARCHITECTURAL FINISHES

- Verde Alpi Green Marble
- Wall-Hung Concealed WC
- Brushed Gold Monobloc Faucet
- Terrazzo Mosaic Floor
- Backlit Fluted Mirror

SPATIAL & TECHNICAL HIGHLIGHTS

- Monolithic custom washbasin carved from a single solid block of Verde Alpi marble
- Concealed in-wall plumbing cistern with brushed brass dual-flush architectural faceplate
- Vertical shadowline perimeter lighting washing textured wallpaper with dramatic accent graze

SURFACES

Large Porcelain Slabs & Fluted Tile

FITTINGS

Brushed Gunmetal & Matte Black

Detailing: Linear concealed tile-insert drain channels and frameless toughened glass screens keep visual sightlines razor-sharp.

SANITARYWARE

Concealed Cisterns & Wall-Hung Pans

LIGHTING

IP65 Warm 3000K Backlit Vanity



EN-SUITE VANITY · HALO MIRROR & FLOATING STONE BASIN



WALK-IN SHOWER & NICHE DETAIL



SCULPTURAL POWDER ROOM

COMMERCIAL WORKPLACE · CORPORATE SUITE

Executive Presence & Acoustic Precision

Engineered for high-stakes corporate deliberations and seamless international video conferencing, this executive boardroom synthesizes commanding presence with acoustic comfort and ergonomic excellence.

A bespoke 14-seat monolithic conference table featuring an Italian marble inset slab is equipped with flush-integrated gooseneck conference microphones and concealed cable raceways. Smoked walnut millwork with fluted acoustic paneling conceals AV infrastructure while framing an ultra-high-definition presentation screen and open curated display shelving. Warm cove perimeter lighting and herringbone parquet flooring cultivate an authoritative yet welcoming environment.

MATERIALITY & ARCHITECTURAL FINISHES

- Bookmatched Marquina Marble
- Slatted Smoked Walnut Battens
- Herringbone Walnut Parquet
- Top-Grain Conference Leather
- Bronze AV Trims

SPATIAL & TECHNICAL HIGHLIGHTS

- 14-seat boardroom table with flush motorized connectivity boxes and integrated boundary mics
- Ultra-wide 4K presentation display seamlessly framed by acoustic walnut wall battens
- Multi-layer acoustic ceiling baffle assembly achieving optimal RT60 reverberation control

TYPOLGY

Executive Conference Hall

CAPACITY

14-Seat Boardroom Table

JOINERY

Fluted Smoked Walnut Millwork

TECHNOLOGY

Integrated AV Screen & Tabletop Mics

Acoustic Engineering: Fluted wall battens, recessed acoustic ceiling coves, and flush acoustic doors balance reverberation time (RT60), guaranteeing exceptional speech intelligibility.



EXECUTIVE BOARDROOM · 14-SEAT MARBLE CONFERENCE TABLE, ACOUSTIC WALL JOINERY & INTEGRATED AV DISPLAY

SCHEMATIC PHASE · FREEHAND IDEATION

From Conceptual Sketch to Constructed Reality

Every rigorous architectural interior originates in the disciplined freedom of freehand sketching. Before transitioning to digital CAD drafting, volumetric massing, daylighting angles, and indoor-outdoor thresholds are explored through rapid perspective studies.

This perspective sketch explores the architectural massing of a contemporary two-story villa: cantilevered upper suites, deep solar shading overhangs, expansive ground-level glazing, and integrated poolside terraces. This conceptual vision directly informs the dimensioned floor plans, structural sections, and bespoke joinery packages that follow.

MATERIALITY & ARCHITECTURAL FINISHES

Hand-Drawn Perspective Drafting

Prismacolor Architectural Markers

Technical Fineliner Ink

Isometric Volume Grids

Drafting Vellum

SPATIAL & TECHNICAL HIGHLIGHTS

- Early volumetric concept sketch studying sun angles and overhang depths for tropical climate
- Exploration of cantilevered terraces, water reflection basins, and arrival threshold hierarchy
- Tactile material delineation tested freehand before advancing into parametric CAD & 3D

MEDIUM

Freehand Perspective Sketch

TYPOLOGY

Modern Cantilevered Villa

FOCUS AREA

Volumetric Balance & Terraces

CAD TRANSLATION

Ground Plans, Sections & Details

Methodological Continuity: Freehand ideation unlocks spatial proportion and massing clarity, which are subsequently codified into millimeter-precise AutoCAD construction documentation.

SCHEMATIC IDEATION · FREEHAND STUDY

Architectural Perspective Massing

HAND SKETCH




Freehand architectural perspective exploring cantilevered upper volumes, shaded poolside terrace, and glazing thresholds.

CAD TRANSLATION · FLOOR PLAN

AutoCAD 1:50 Dimensioned Plan

AUTOCAD 1:50

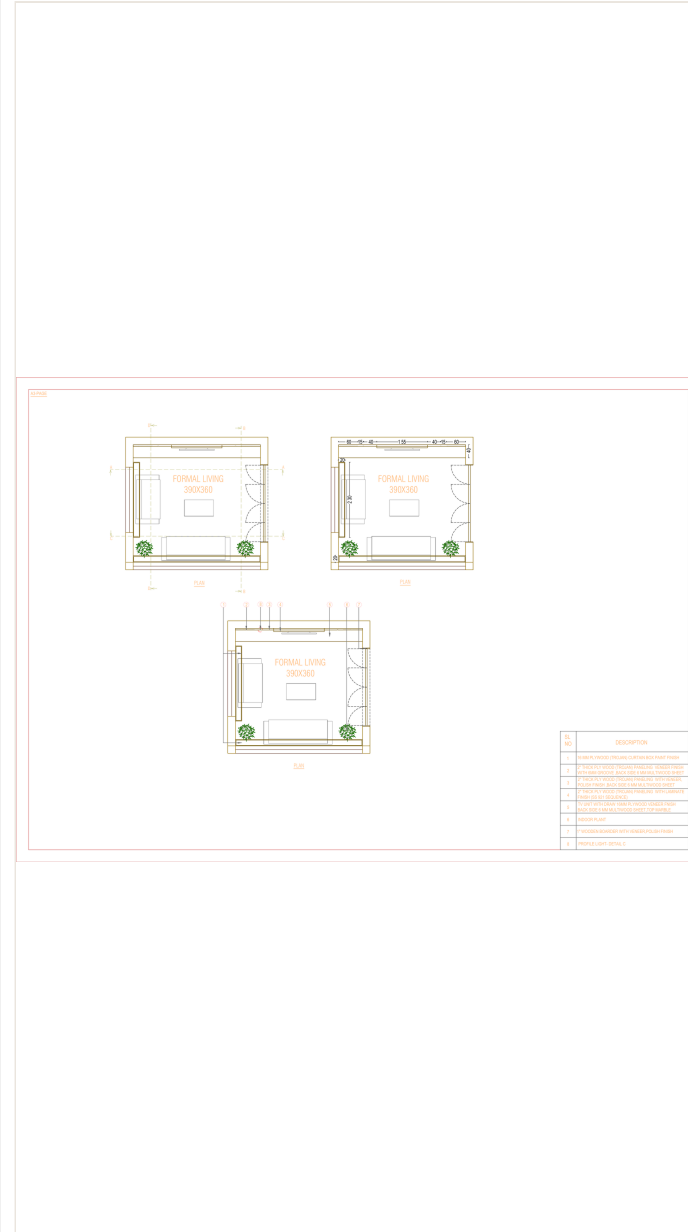

Precise 2D translation documenting structural masonry, circulation corridors, and interior fitout boundaries.

Formal Living Room *Layout & Section AA*

Architectural working drawings drafted to 1:50 scale specifying structural perimeter envelope, circulation clearances, modular seating offsets, and media wall paneling.

SHEET A101 · DIMENSIONED FLOOR PLAN

AUTOCAD 1:50

Formal Living Room Spatial Layout




Dimensioned layout detailing circulation corridors, seating positions, masonry envelope, and fenestration openings.

SHEET A102 · SECTION AA ELEVATION

AUTOCAD 1:50

Transverse Section & Paneling Elevation

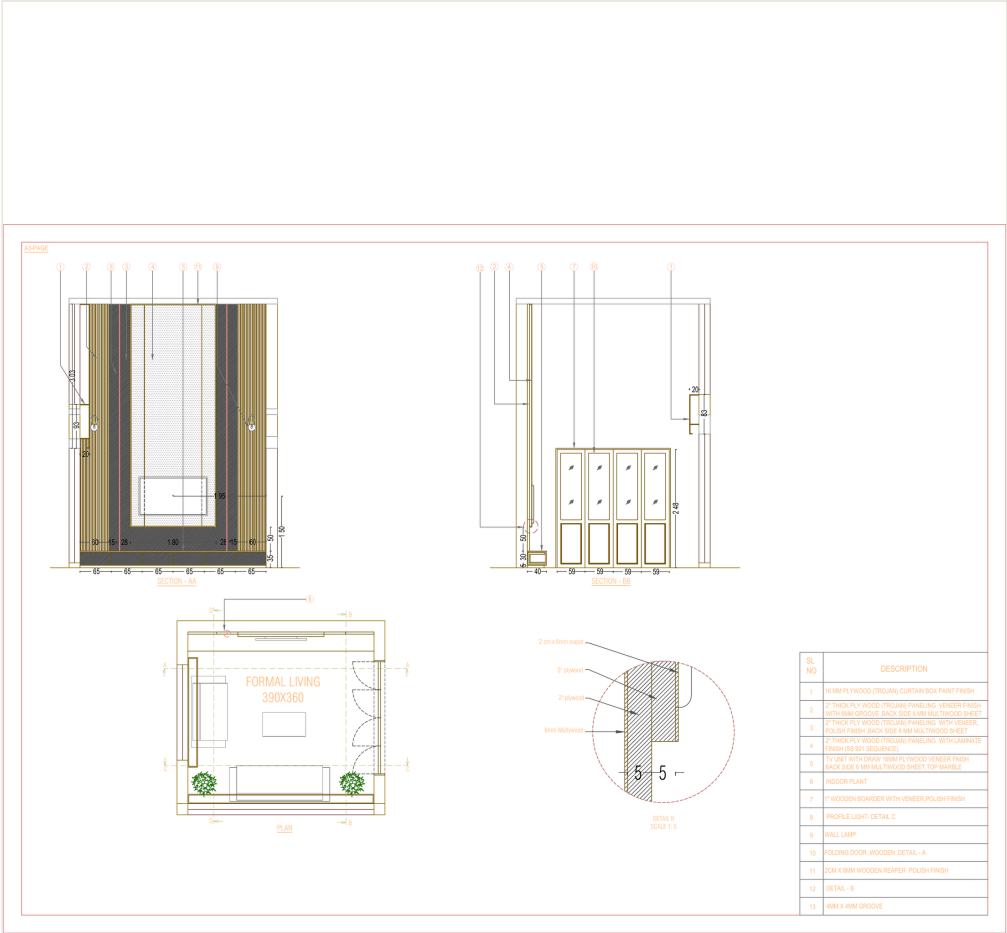


Sectional elevation detailing ceiling drop levels, fluted timber paneling height, wall sconce heights, and conduit routes.

Formal Living *Longitudinal Sections & Glazing*

SHEET A103 · LONGITUDINAL SECTION BB

Longitudinal Section Through Living Suite

AUTOCAD 1:50

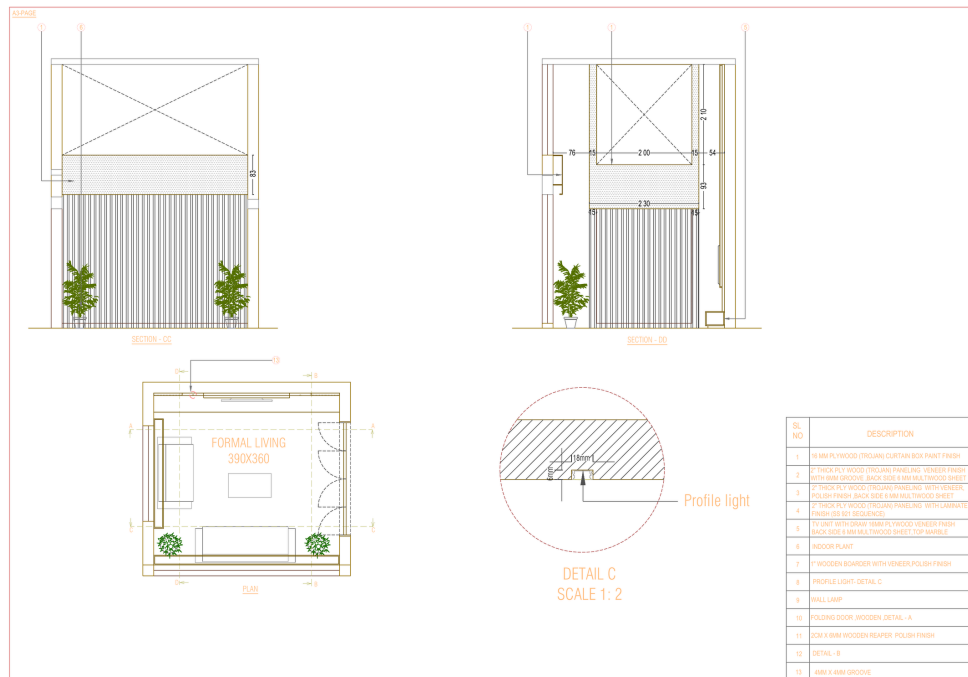


Full-length sectional cut displaying wall cladding substrates, ceiling cove recesses, and skirting interface details.

Vertical sections illustrating lintel datum levels, floor slab drop transitions, acoustic insulation cavity detailing, and structural framing.

SHEET A104 · SECTIONAL ELEVATION CC

Fenestration & Glazing Interface

AUTOCAD 1:50

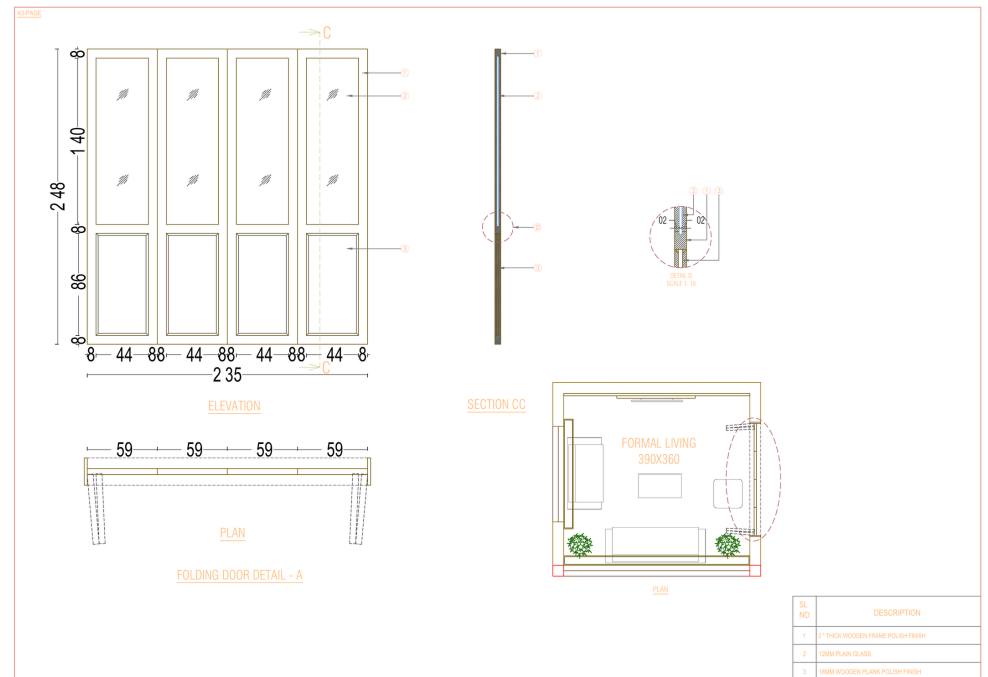


Constructability details showing thermally broken aluminum window profiles, structural mullions, and ceiling reveals.

ARCHITECTURAL CAD SET · 03 OF 06

Biophilic Courtyard *Layout & Console Millwork*

SHEET B101 · PLAN LAYOUT & CONSOLE
Courtyard Floor Plan & Joinery Layout

AUTOCAD 1:50

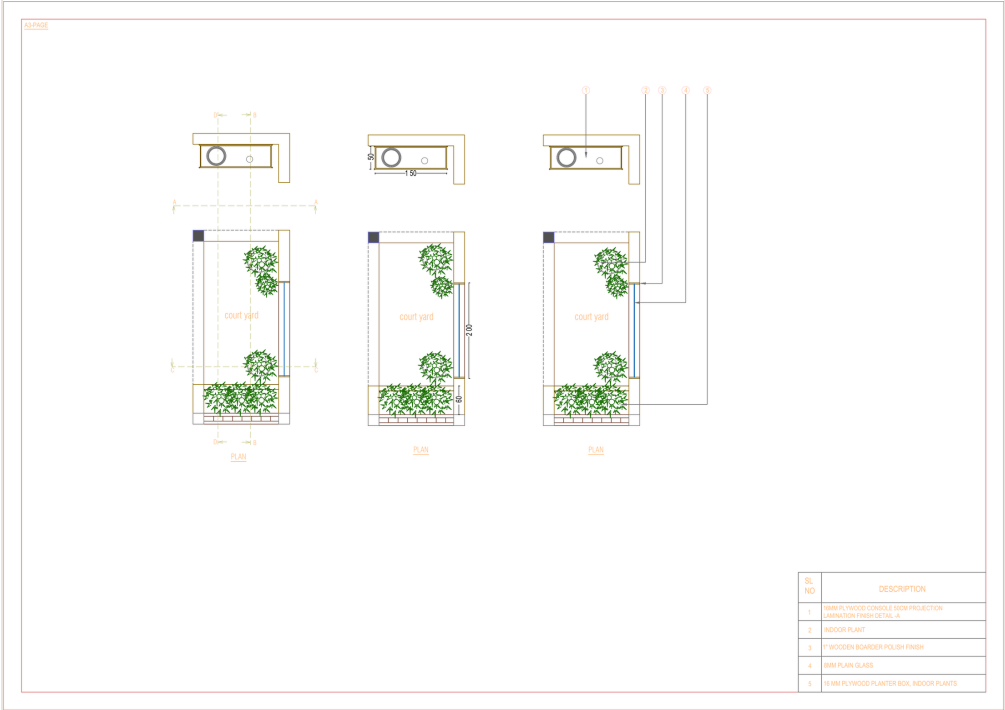

Floor plan detailing courtyard perimeters, stone paving boundaries, and custom multi-compartment plywood console.

SHEET B102 · COURTYARD CROSS SECTIONS
Transverse Sections AA & BB

AUTOCAD 1:50



Vertical sections specifying ceiling skylight opening, double-height light shaft geometry, and planter waterproofing.


Courtyard Enclosure & Planter Drainage

Constructability package detailing planter sub-base soil filtration, rainwater drainage scuppers, and sliding partition enclosure systems.

SHEET B103 · LONGITUDINAL SECTIONS CC & DD

AUTOCAD 1:50


Planter Soil Bed & Drainage Profiles

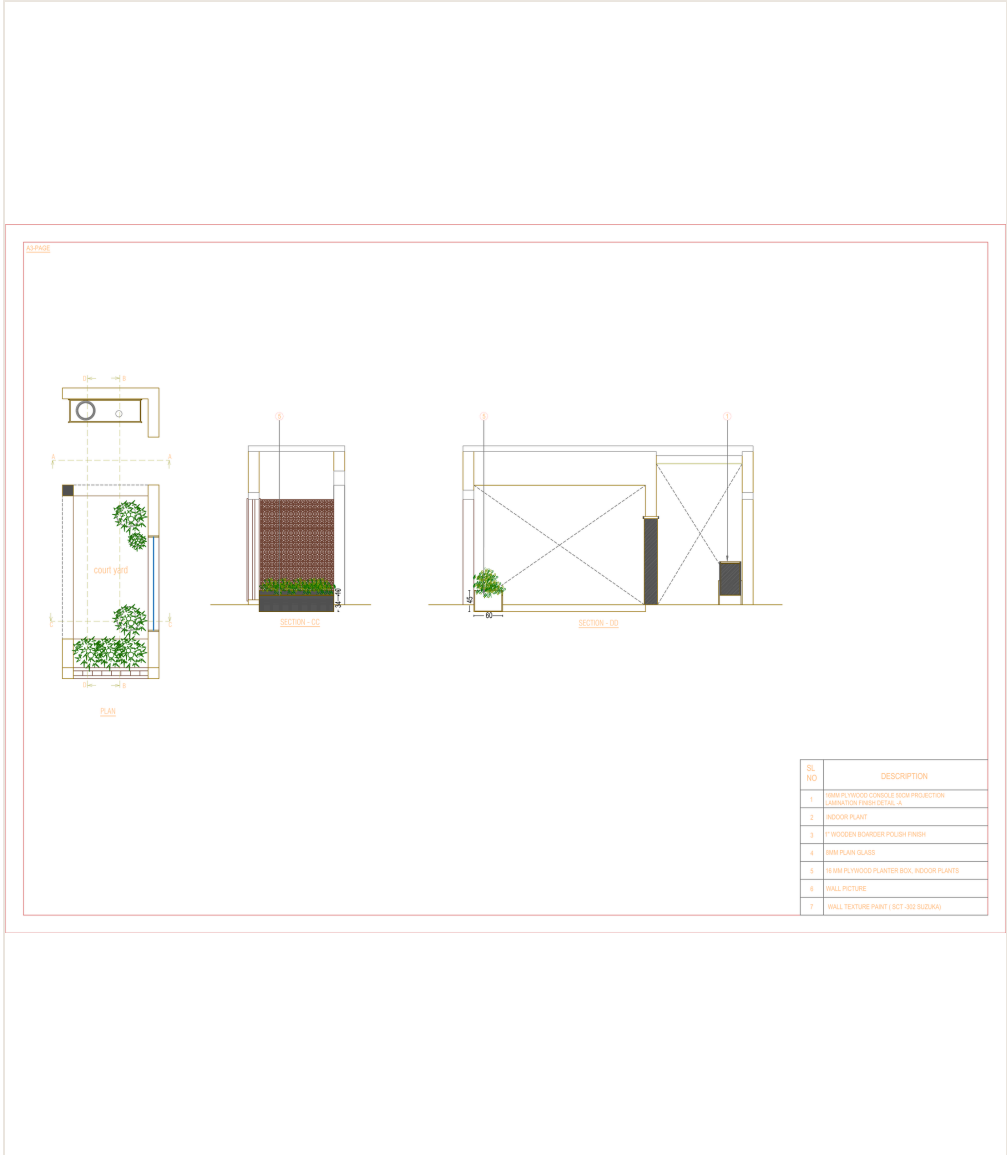

SHEET B104 · ENCLOSURE & SLIDING FENESTRATION

AUTOCAD 1:50

Sliding Glass Partitions & Thresholds

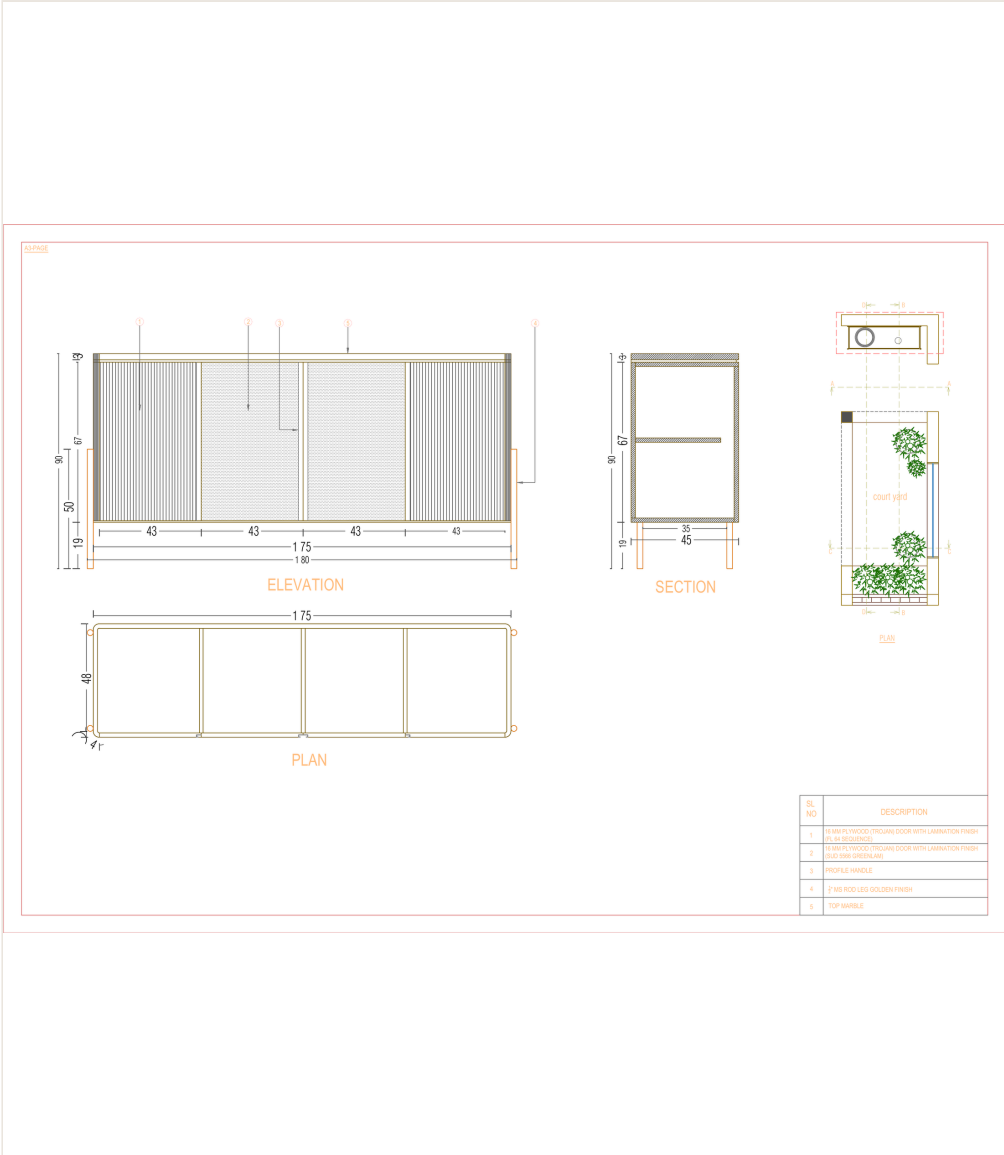

JOINERY PRODUCTION PACK · 05 OF 06


Master Suite 4 Wardrobe & Accent Wall

Joinery shop drawings specifying carcass divisions, Blum soft-close hardware, integrated LED channels, and tactile finish swatches.

DETAIL SHEET J201 · MASTER WARDROBE

JOINERY SHOP DETAIL

Full-Height Master Wardrobe Elevation

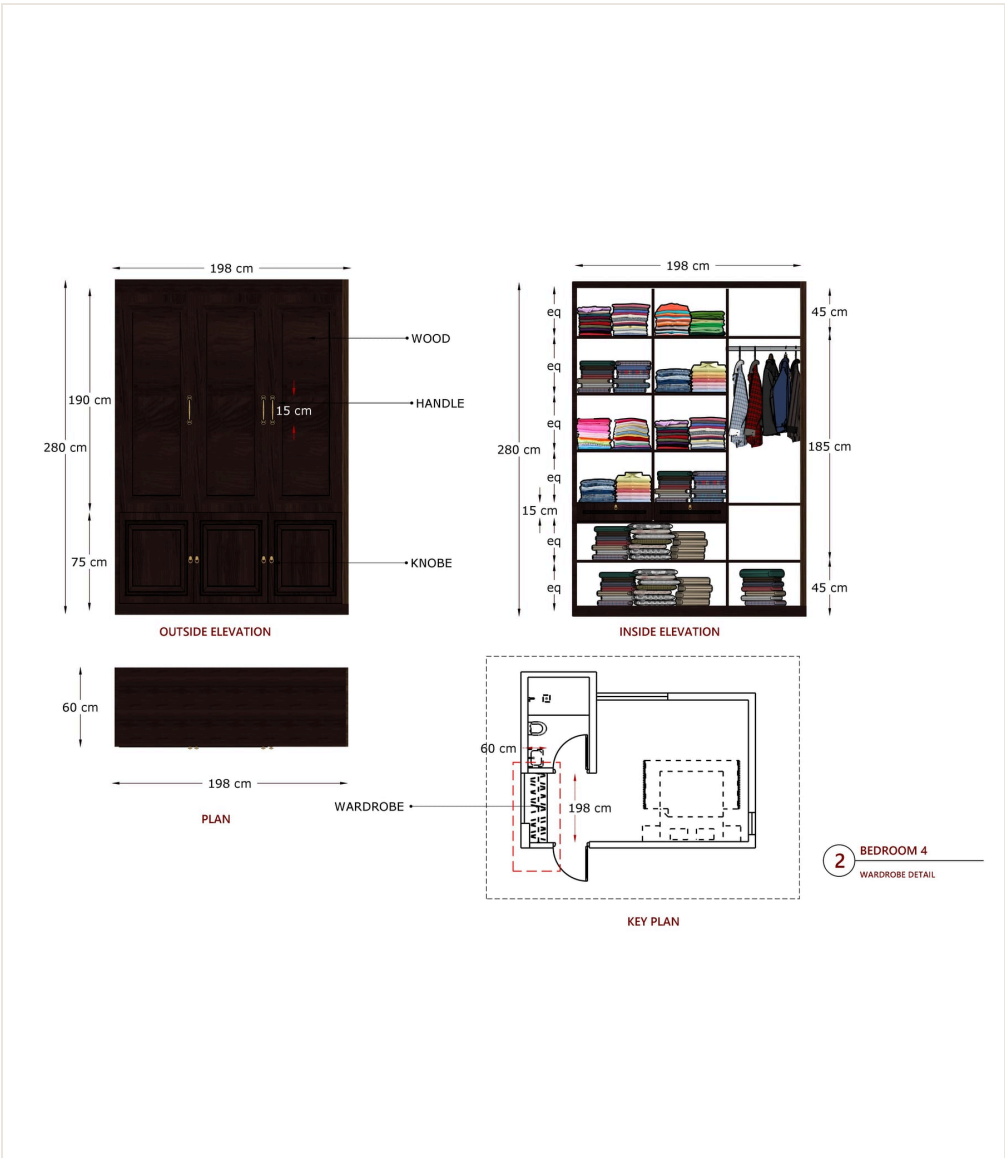


Shop drawing detailing carcass thicknesses, hanging rails, accessory drawers, handle recesses, and integrated LED extrusion.

DETAIL SHEET J202 · HEADBOARD & ACCENT WALL

JOINERY SHOP DETAIL

Headboard Paneling & Beverage Station

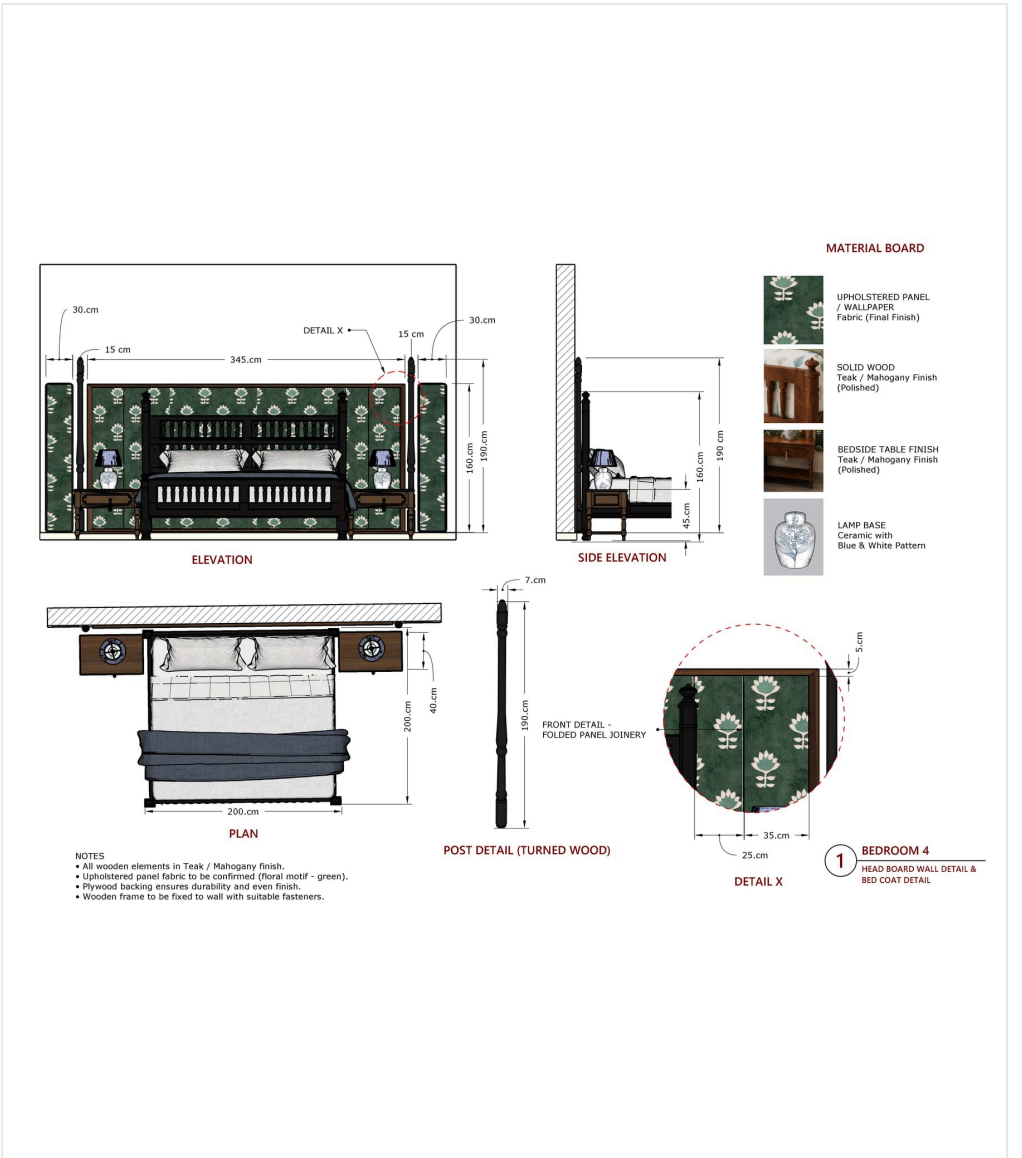

Detailed wall paneling elevation with recessed niche for tea station, integrated electrical points, and approved finish board.

JOINERY PRODUCTION PACK · 06 OF 06


Contemporary Suite 2 Millwork & Bed Detailing

Production drawings detailing carcass construction, edge banding, structural bed frame supports, and floating nightstand integration.

DETAIL SHEET J203 · INTERNAL WARDROBE MILLWORK

JOINERY SHOP DETAIL

Wardrobe Internal Sections & Divisions

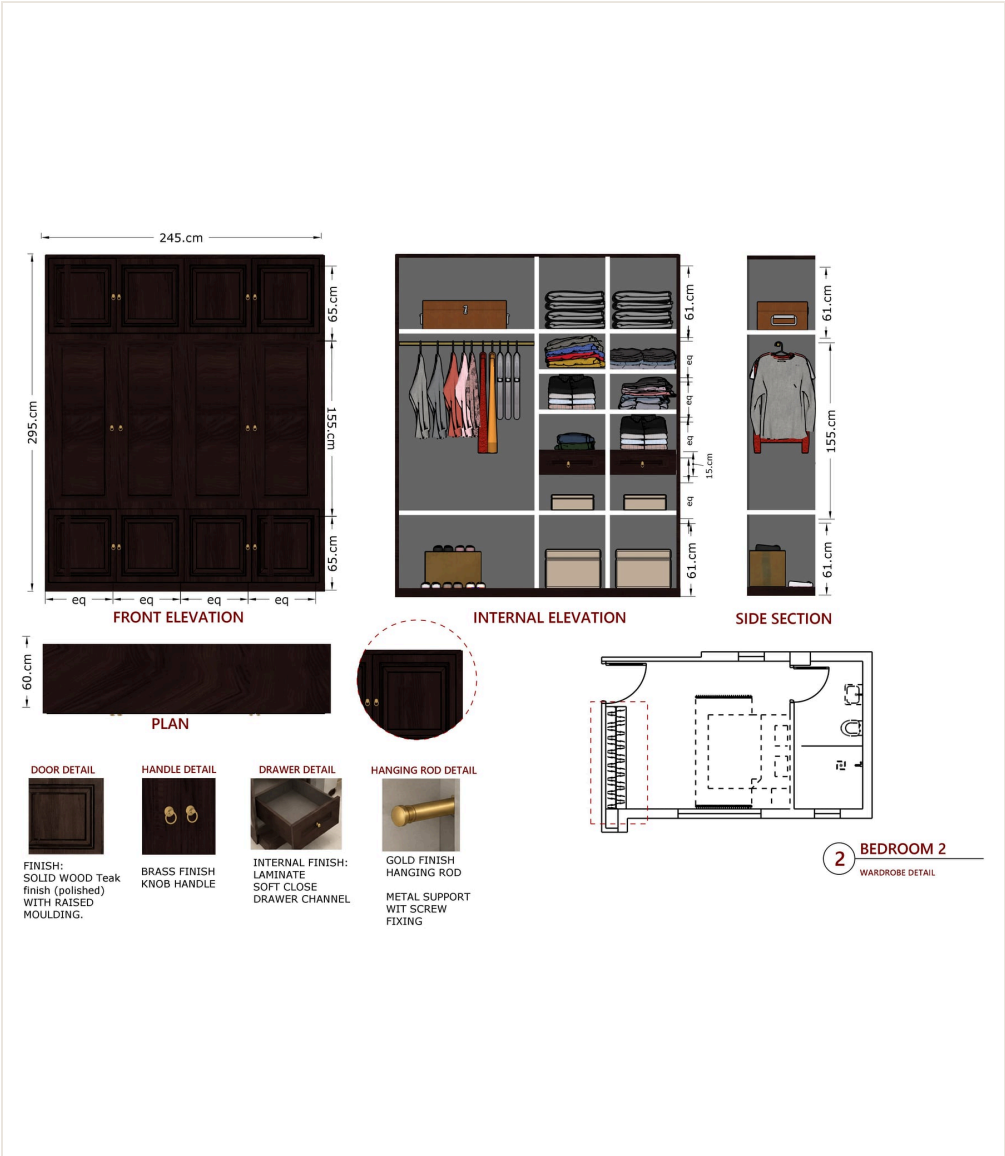


Detailed section through wardrobe units illustrating 18mm marine ply carcass, shelf spacing, and drawer slide positions.

DETAIL SHEET J204 · BED COT & NIGHTSTAND

JOINERY SHOP DETAIL

Bed Platform & Cantilever Nightstand

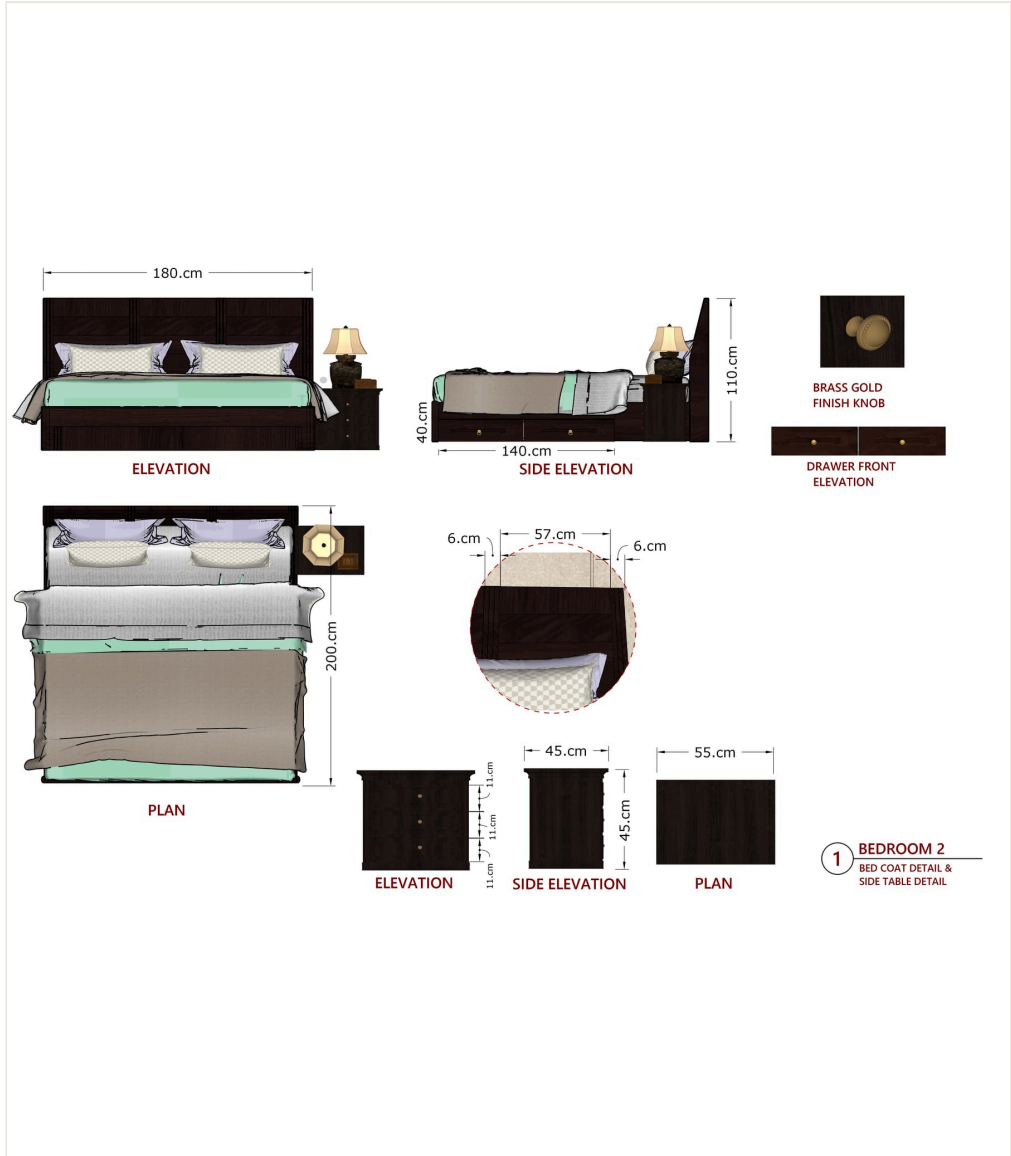

Plan, front elevation, and cross-section of platform bed cot with integrated floating cantilever nightstand and headboard.

Professional Experience

Junior Interior Designer

AlHawaj Architect & Builders · Calicut

Coordinating multi-disciplinary teams across residential villas and commercial developments. Managing space planning, 3D visualization, and cost-efficient client specifications.

Interior Designer

Theyyampattil Homesoul Interior · Calicut

Developed mood boards, furniture plans, and photorealistic 3D perspectives. Created detailed 2D production drawings for custom millwork and supervised site execution schedules.

Professional Focus

- Residential & Living Space Planning
- Bespoke Millwork & Joinery Detailing
- Photorealistic 3D Architectural Visualization

Academic Education

Diploma in Interior Design

Alagappa University, Tamil Nadu · 2024–2025

Specialized in interior architecture, 3D computer rendering, and technical detailing.

Bachelor of Arts in Sociology

Calicut University, Kerala · 2017–2020

Focused on human behavior, community environments, and socio-spatial interaction.

Software Stack

AutoCAD

Revit BIM

SketchUp

3ds Max

Enscape

Lumion

D5 Render

Adobe Photoshop

Adobe InDesign

Adobe Illustrator

Procreate

Microsoft Office

Let's Collaborate

Open to junior interior designer positions, collaborative architectural projects, and design consultations worldwide.

Email: faihafaisal668@gmail.com

Phone: +91 9544466908

LinkedIn: [linkedin.com/in/faiha-faisal](https://www.linkedin.com/in/faiha-faisal)

Location: Calicut, Kerala, India

Languages: English, Hindi, Tamil, Malayalam

Faiha Faisal

THANK YOU FOR REVIEWING MY PORTFOLIO