


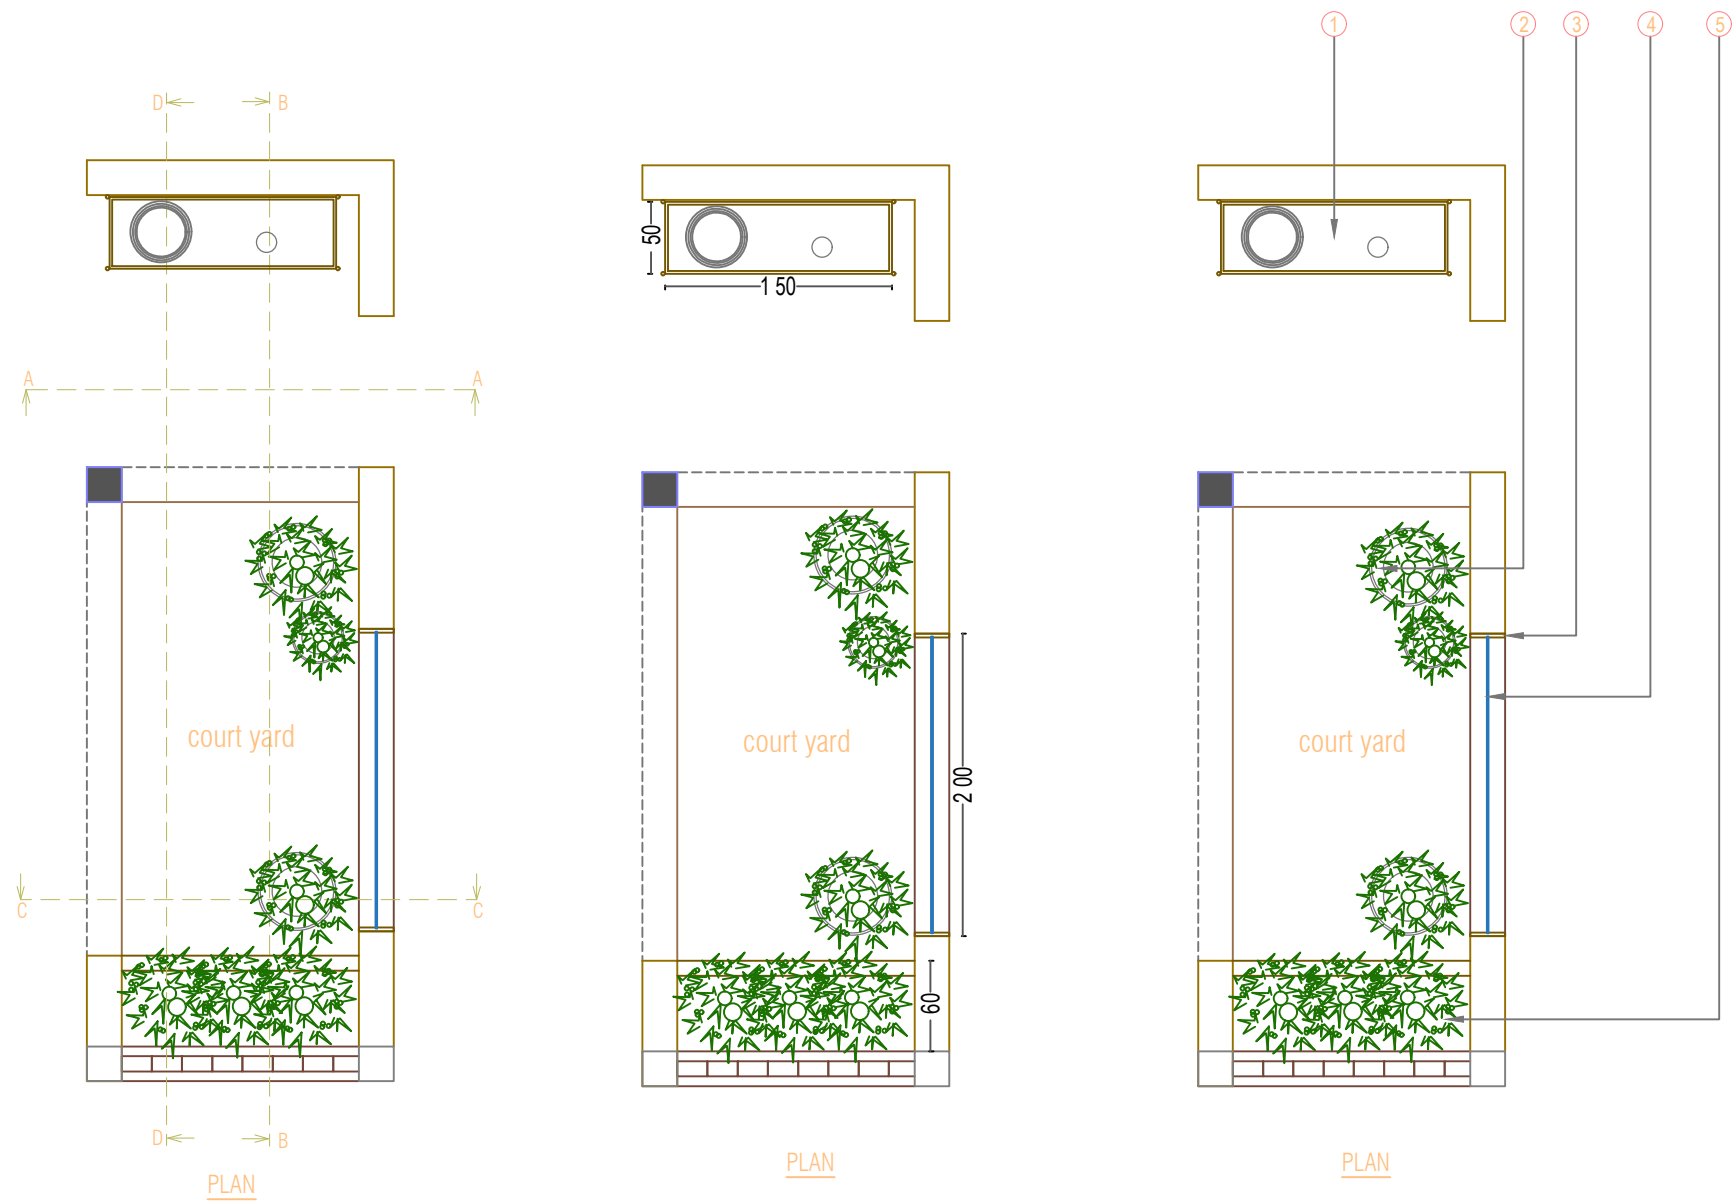

SL NO	DESCRIPTION
1	16MM PLYWOOD CONSOLE 50CM PROJECTION LAMINATION FINISH DETAIL -A
2	INDOOR PLANT
3	1" WOODEN BOARDER POLISH FINISH
4	8MM PLAIN GLASS
5	16 MM PLYWOOD PLANTER BOX, INDOOR PLANTS